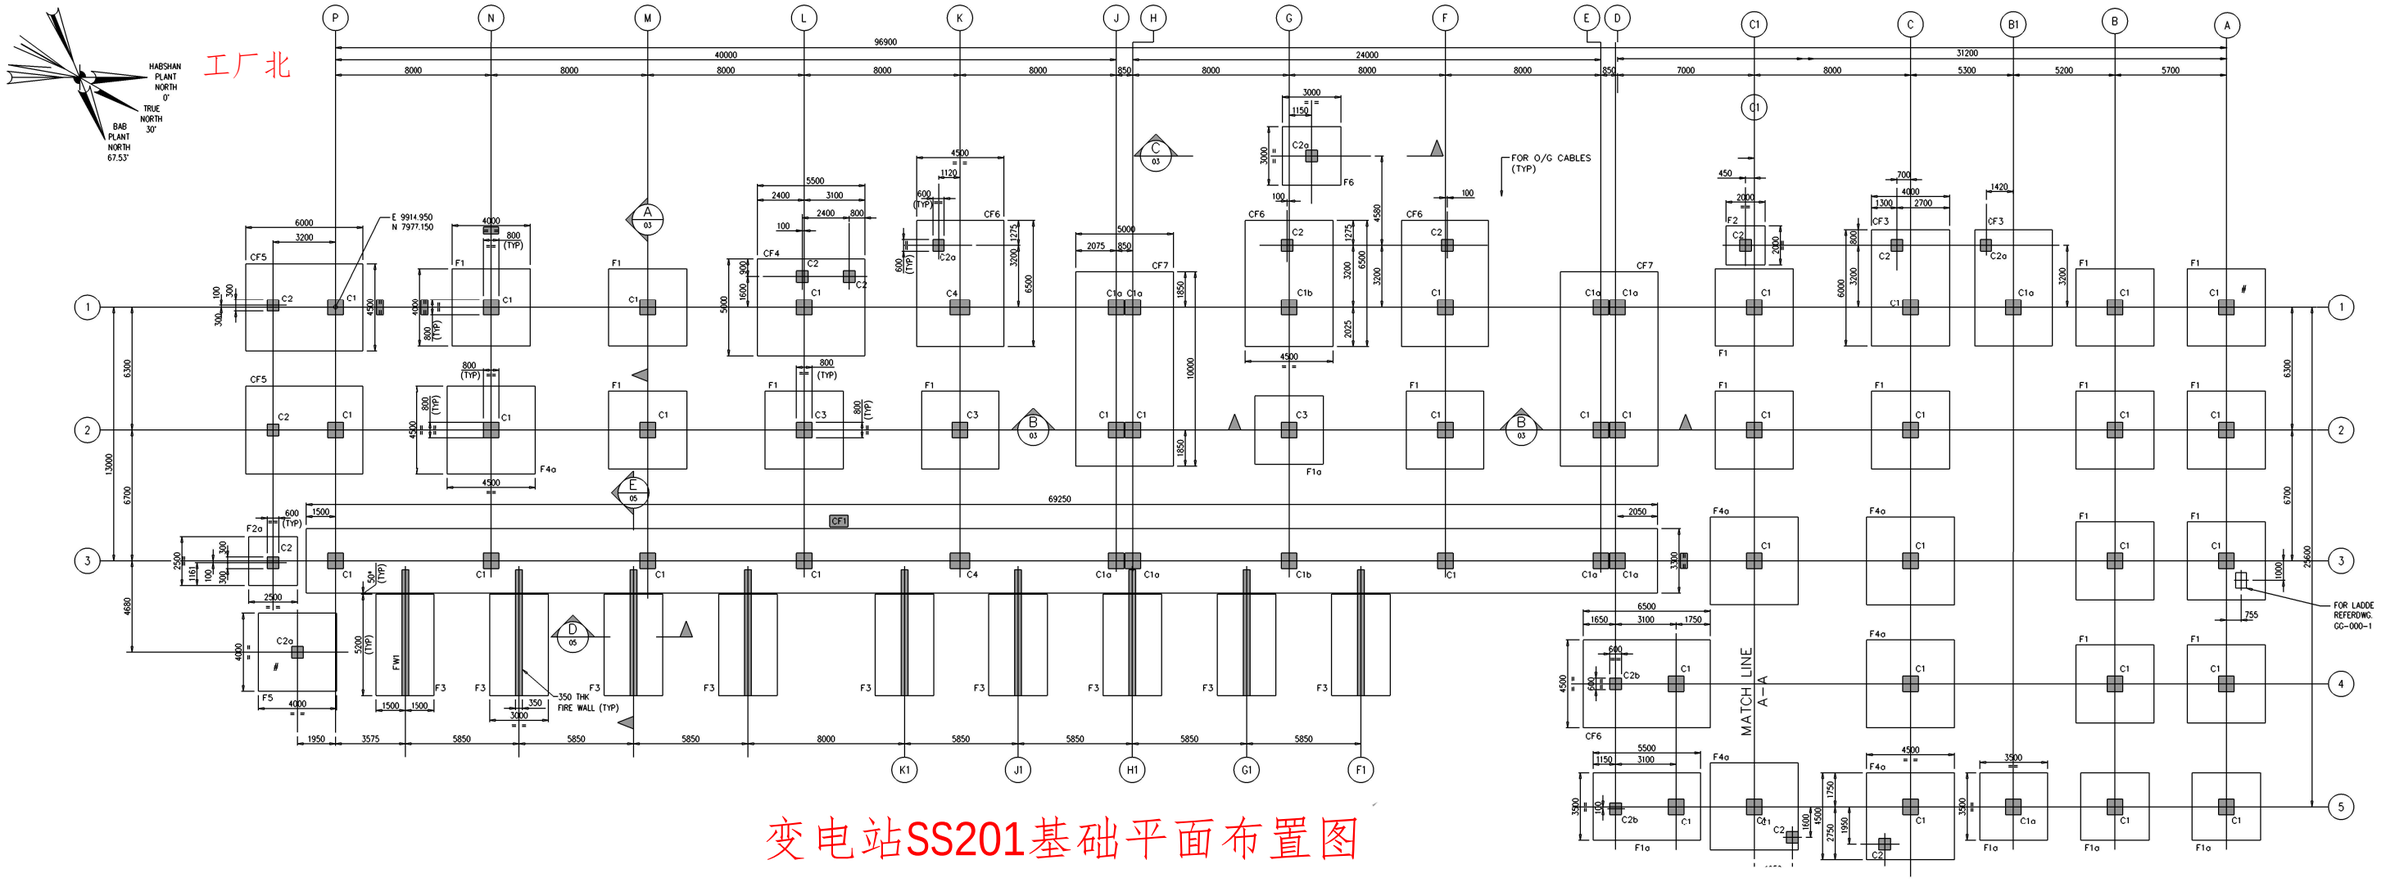

变电站SS201基础平面布置图